



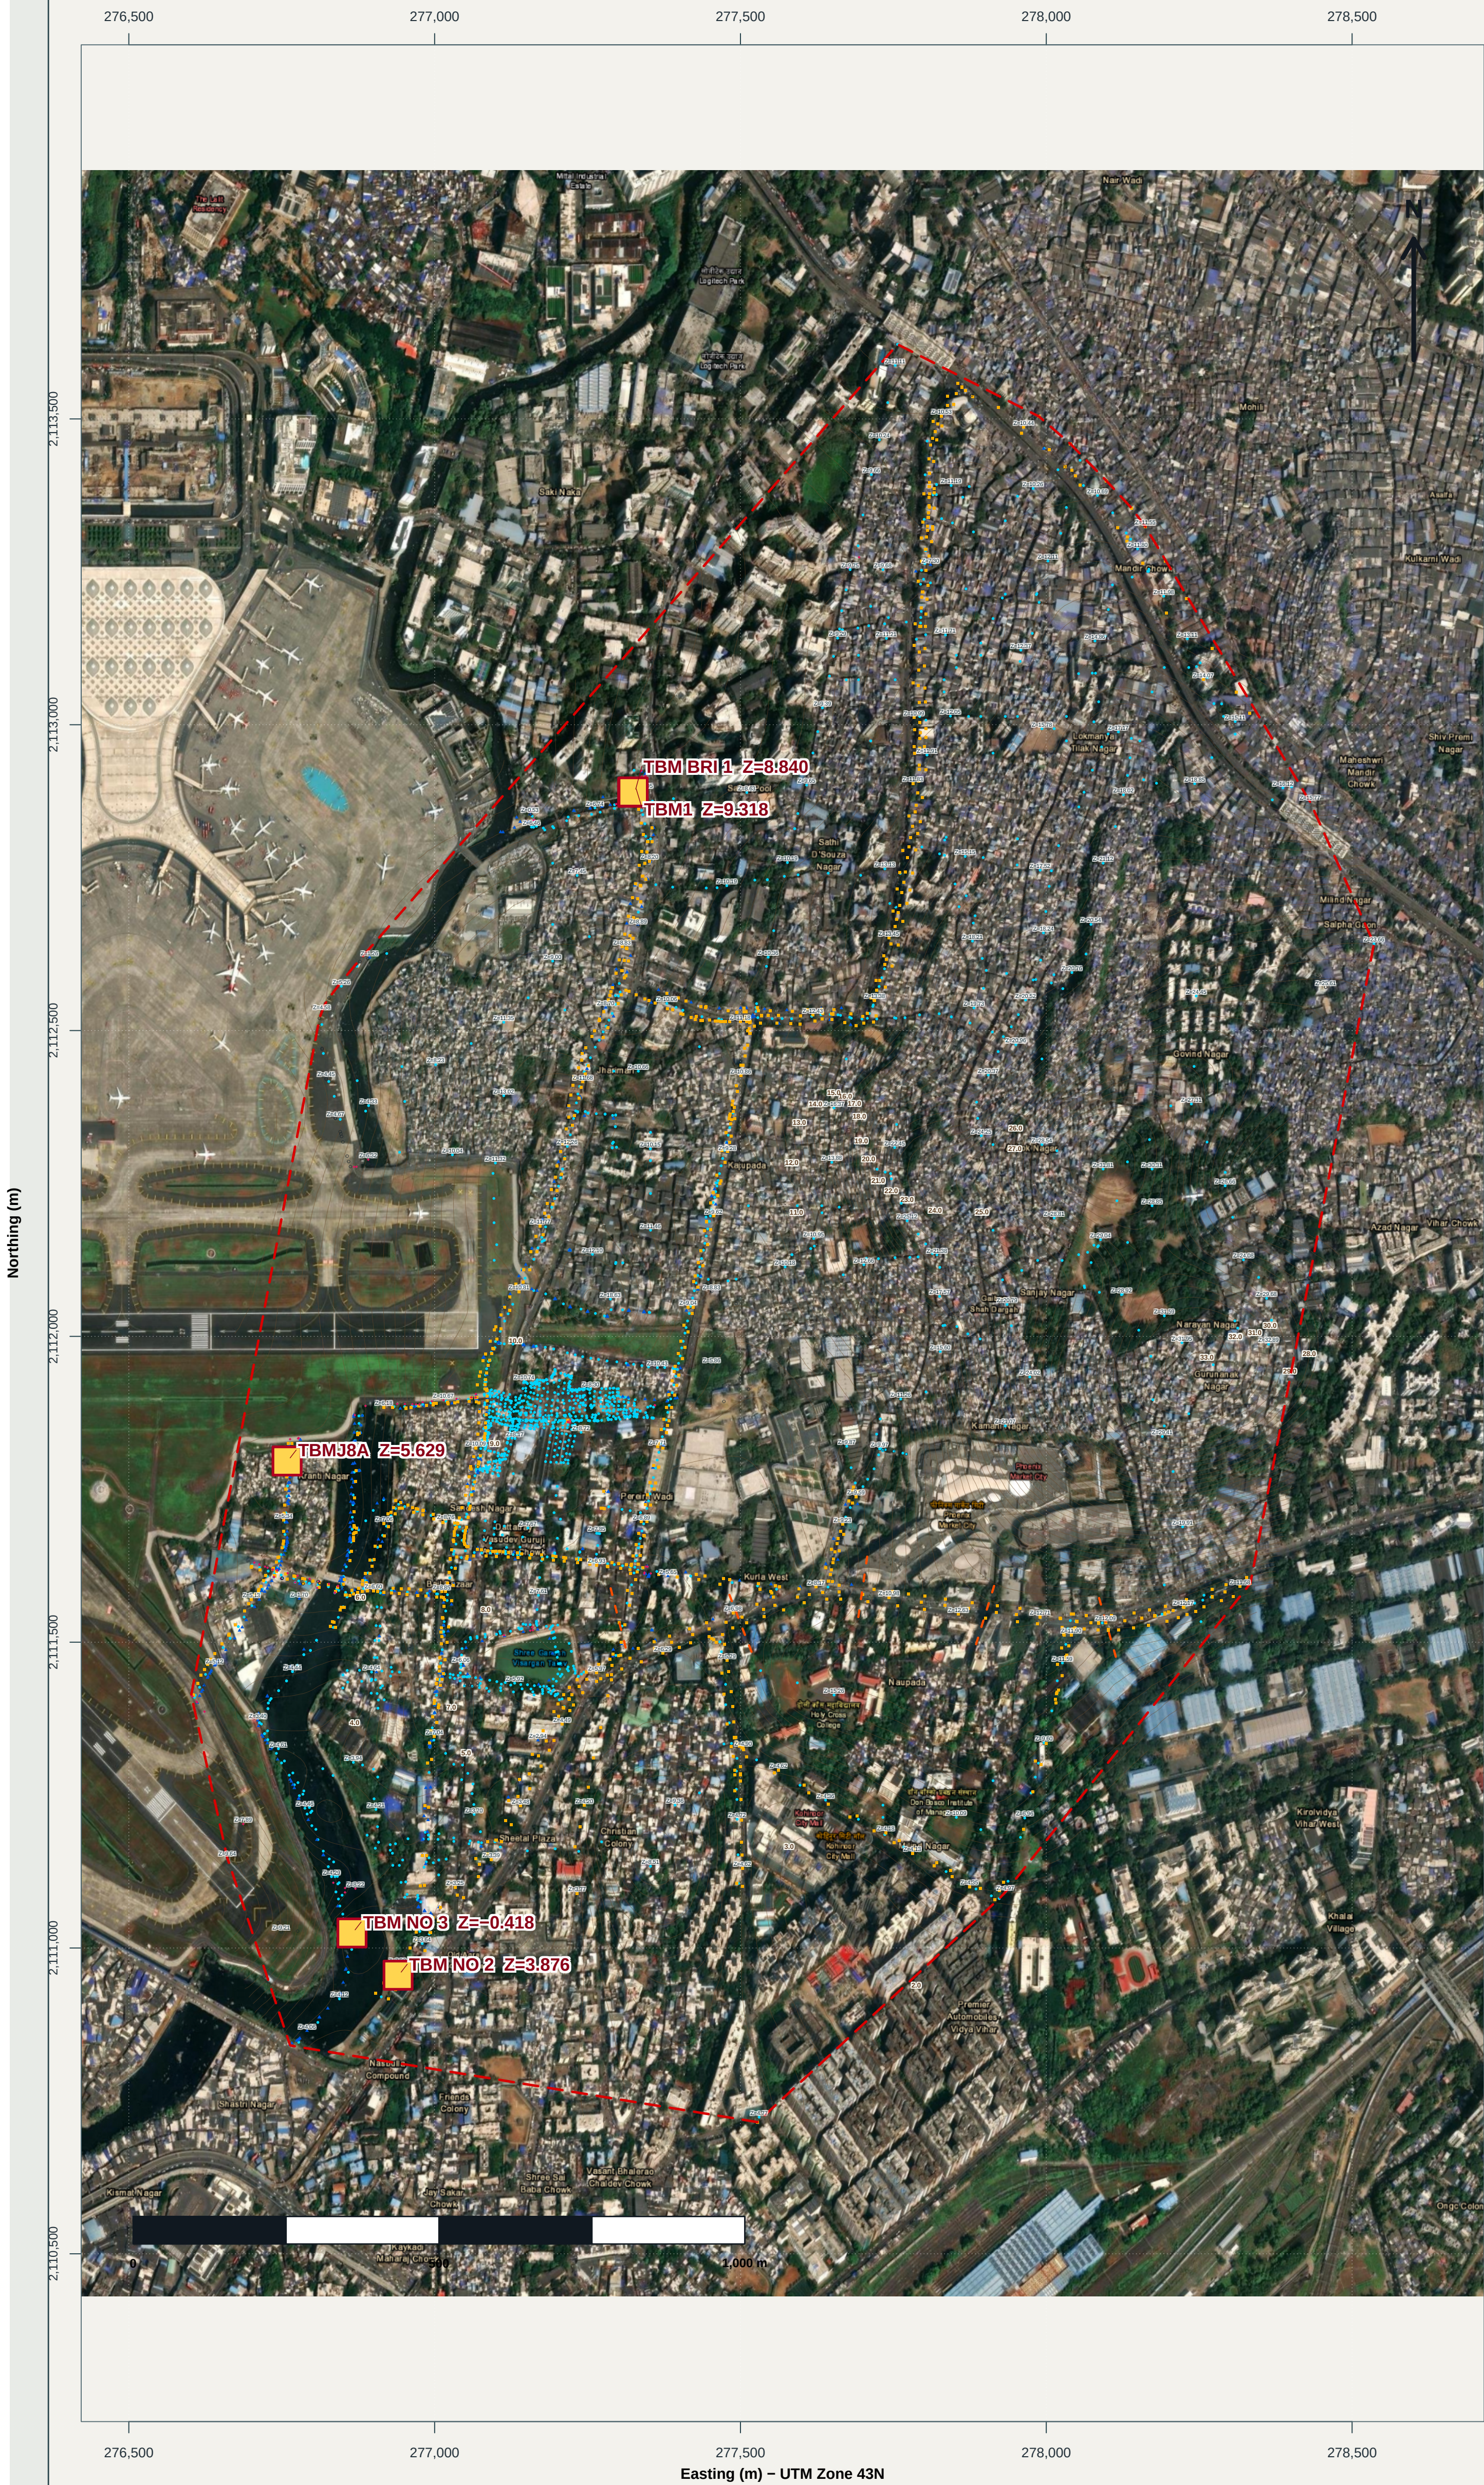

OVERVIEW MAP

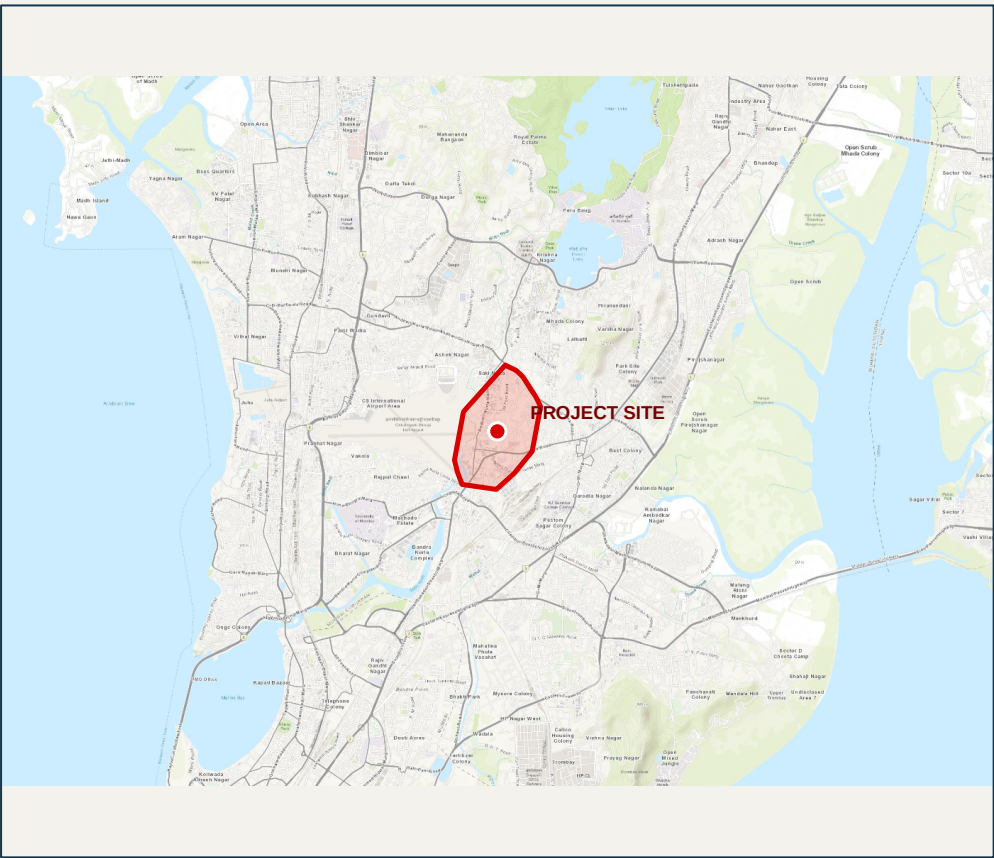

MAP LEGEND

- Ground / edge levels
- Drainage / watercourse
- Road / hardscape
- Structures / crossings
- BM / TBM control
- Other surveyed features
- Survey coverage boundary
- 0.5 m contours
- Road cross-section lines

SCOPE OF WORK

- DGPS (RTK-based) survey of ground level across the off-site catchment area.
- Grid-based spot levels at regular intervals across open/sloping terrain.
- Closer-interval spot levels and cross-sections at drainage features, nals, watercourses, road crossings and culverts.
- Capture of physical features influencing drainage: embankments, retaining structures, culverts/outfalls and other hydraulically significant features.

CONTROL POINTS

NAME	EASTING	NORTHING	Z (m)
TBM NO 2	276940.22	2110955.52	3.876
TBM NO 3	276864.88	2111024.58	−0.418
TBMJ8A	276758.72	2111796.24	5.629
TBM BRI 1	277323.75	2112889.71	8.840
TBM1	277324.55	2112890.13	9.318

Basemap credits: Esri and contributors. Survey overlay: KP Associates. 4,125 observations | WGS 84 / UTM Zone 43N | 500 m grid | spot Z labels spatially thinned; contours labelled at 1 m. Scale valid only at A1.

NAME OF WORK

Land Survey Work for proposed warehouse on plot bearing CTS Nos. 67, 68, 69, 70 & 71 at Village Kurla-1, L-Ward, Andheri-Kurla Road, Kurla (West), Mumbai.

CONSULTANT

KP ASSOCIATES

Plot No. 362, Sector E, CIDCO, Behind Indo German Tool Room, Chhatrapati Sambhajanagar, Maharashtra 431003, India

CLIENT

XSIO URBAN LOGISTICS PVT. LTD.

SHEET: 02 / 2

SCALE: 1:6,000 @ A1

SIZE: A1 PORTRAIT

BASEMAP: ESRI SATELLITE HYBRID

DATE: 05 OCT 2026